
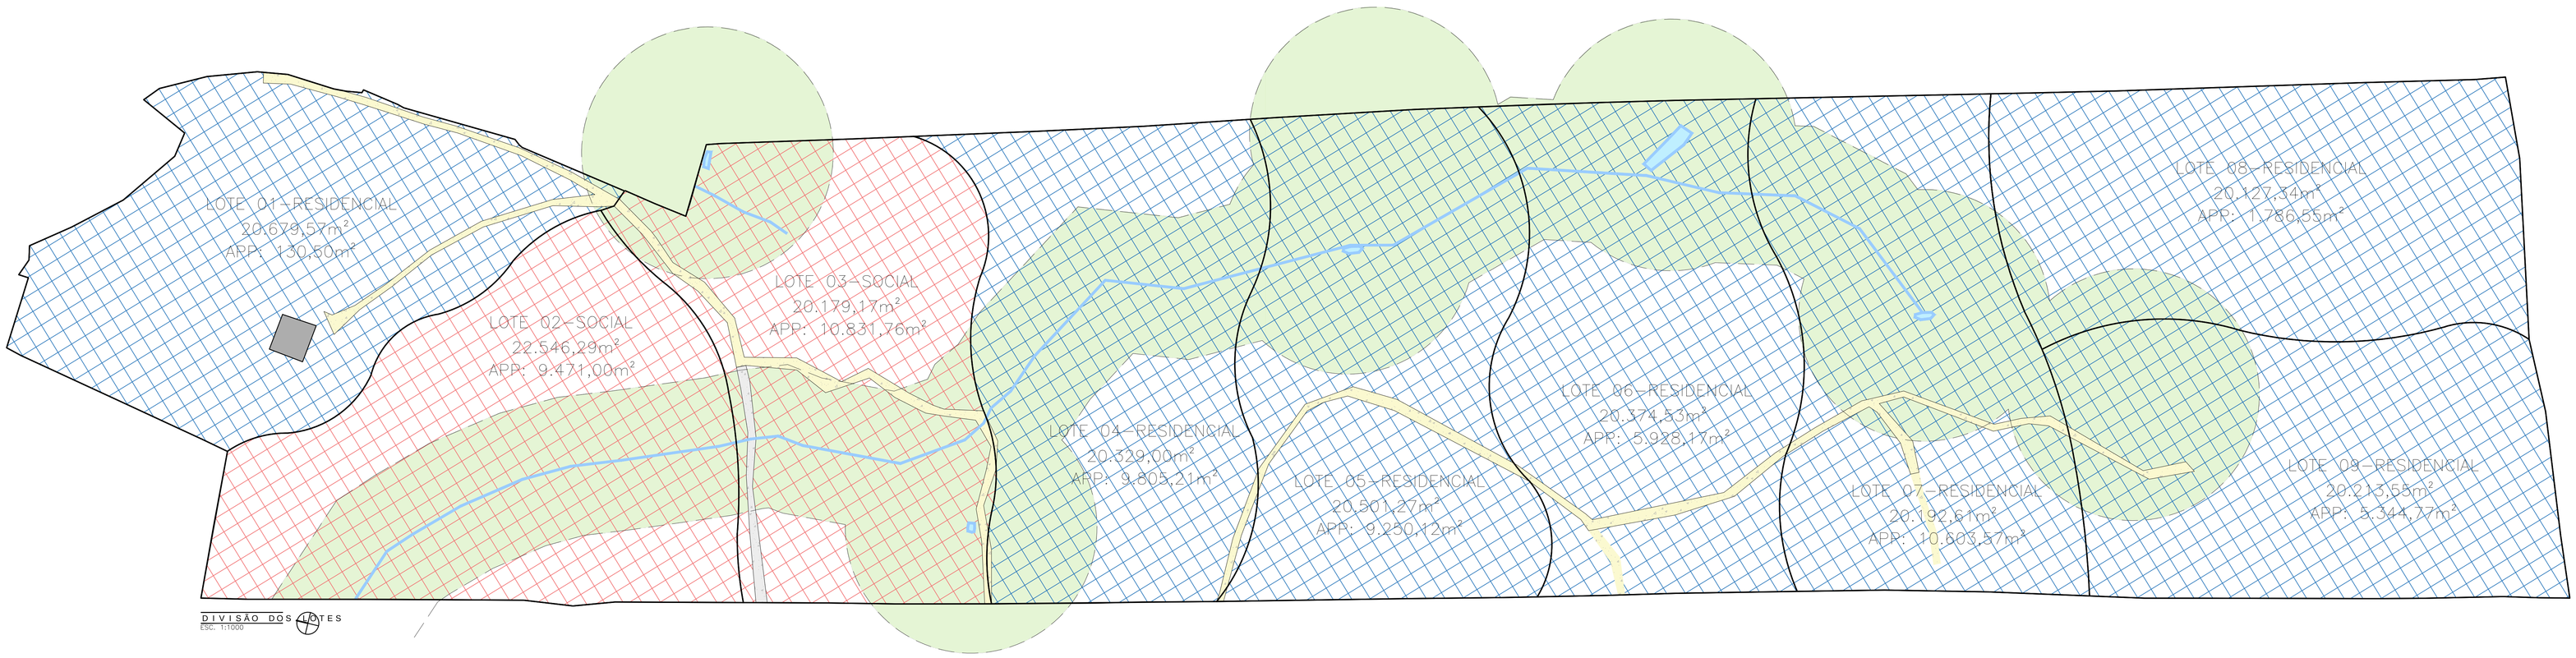


DIVISÃO DOS LOTES
ESC. 1:1000

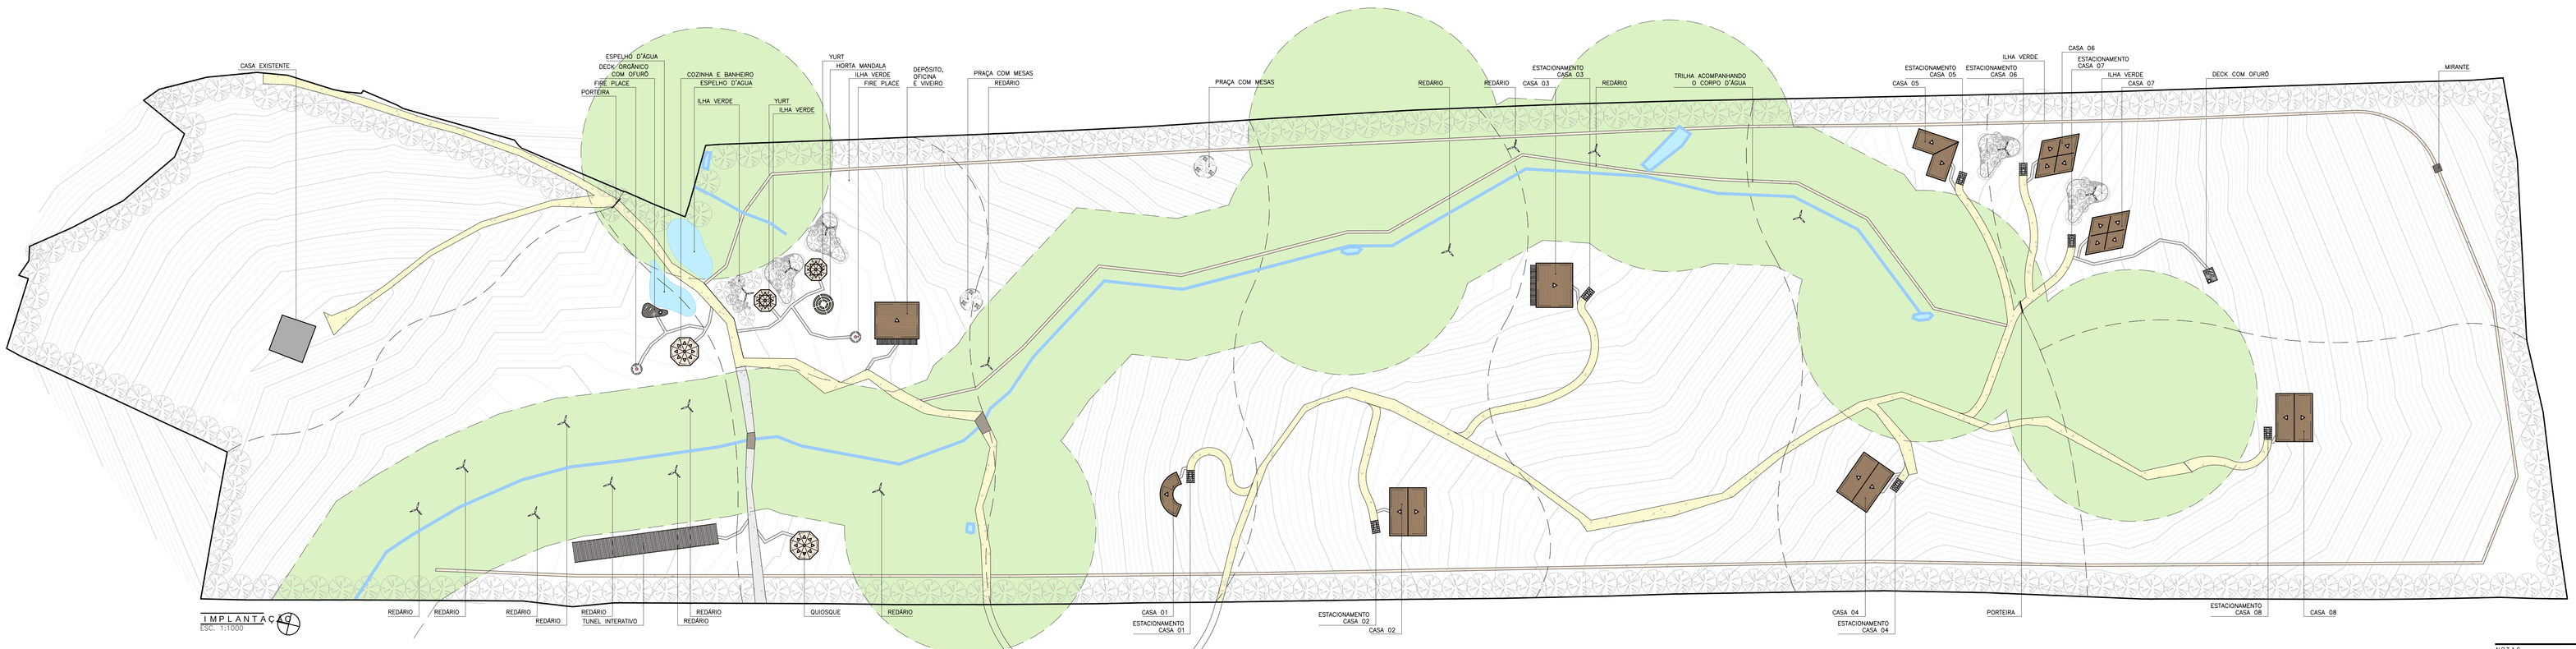

IMPLANTAÇÃO
ESC. 1:1000

QUADRO DE ÁREAS		
LEG.	TIPO	ÁREA (M²)
	ESTRADA DE VEÍCULOS	4.579,10
	ESTRADA DE PEDESTRES	636,60
	TRILHA	2.185,80
01	CASA EXISTENTE	
02	ESPELHO D'ÁGUA	482,25
03	DECK ORGÂNICO COM OFURÔ	38,80
04	FIRE PLACE – 15,20m²	30,40
05	QUIOSQUE – 78,55m²	157,10
06	HORTA MANDALA	21,40
07	YURT – 38,50	77,00
08	TUNEL INTERATIVO	460,80
09	DEPÓSITO, OFICINA E VIVEIRO	208,00
10	REDÁRIO – 9,50m²	180,50
11	PRAÇA COM MESAS – 63,65m²	127,30
12	CASA 01	55,65
13	CASA 02	227,50
14	CASA 03	208,00
15	CASA 04	227,50
16	CASA 05	150,20
17	CASA 06	165,00
18	CASA 07	165,00
19	CASA 08	227,50
20	ESTACIONAMENTO CASAS –15,00m²	120,00
21	DECK COM OFURÔ	22,00
22	MIRANTE	9,00
23	ILHA VERDE – 173,30m²	866,50
		11.645,90

NOTAS
- ESSE PROJETO DEVERÁ SER EXECUTADO CONFORME CONTRATO Nº XXXXX
- COTAS EM METROS;
- COTAS DE NÍVEL EM METROS;
- CONFERIR MEDIDAS, ABERTURAS, NÍVEIS E PRUMOS NO LOCAL;
- MEDIDAS EM COTAS PREVALECEM SOBRE O DESENHO;
- ESSE DESENHO DEVE SER IMPRESSO COLORIDO;
- IMPLANTAÇÃO DE TERRENO COM PLANO DE MASSAS ILUSTRANDO ONDE SERÃO AS FUTURAS CONSTRUÇÕES COM INDICAÇÃO DA ÁREA IDEAL;
- POSICIONAMENTO DO TERRENO COM RELAÇÃO A TRAJETÓRIA SOLAR E AS CONSTRUÇÕES POSSÍVEIS (DE ACORDO COM BRIFING E VISITA IN LOCO);
- LEVANTAMENTO DE VENTOS PREDOMINANTES ILUSTRADOS ATRAVÉS DE GRÁFICOS JÁ ENVIADOS POR EMAIL;
- LEVANTAMENTO DAS CHUVAS ILUSTRADOS ATRAVÉS DE GRÁFICOS JÁ ENVIADOS POR EMAIL;
- NÃO HÁ MASSA SIGNIFICATIVA DE VEGETAÇÃO;
- NÃO HÁ TECIDO URBANO SIGNIFICATIVO PRÓXIMO;
- ENTORNO E FLUXOS DESTINADOS PREDOMINANTEMENTE PARA A RESIDÊNCIA;
- ILUSTRAÇÃO DE POSSIBILIDADE DE PAISAGISMO CONFORME PROJETO;
- TERRENO DE TOPOGRAFIA PLANA COM ALTO POTENCIAL AGRICULTÁVEL;
- SISTEMA CONSTRUTIVO IDEAL PARA O TERRENO: ADOBE, PAU A PIQUE OU TIJOLO ECOLÓGICO.

DATA	DESENHO TÉCNICO	AUTORA E RESPONSÁVEL TÉCNICA
29/05/2024	TAUANE RIBEIRO	ARQT. MARIANNA MAR

ARQUIVO: MMARC_AVT_FEDERICO E DIANA_RV02.DWG

COD. DO PROJETO	FASE
XXXXX	ANÁLISE DE VIABILIDADE

01/01

TÍTULO
DIVISÃO DOS LOTES
IMPLANTAÇÃO

PROJETO
SAPUCAÍ MIRIM – MG

CLIENTE
FEDERICO E DIANA

TRABALHO DESENVOLVIDO

MARIANNA MAR
ARQUITETURA & DESIGN ECOLÓGICO
WWW.MMARARQUITETURA.COM | MAR@MMARARQUITETURA.COM.BR | (12) 98219 8423